


Variante A — Lit de concassé et chape stabilisée

Cotes en mètres · esquisse à faire vérifier par un bureau d'études

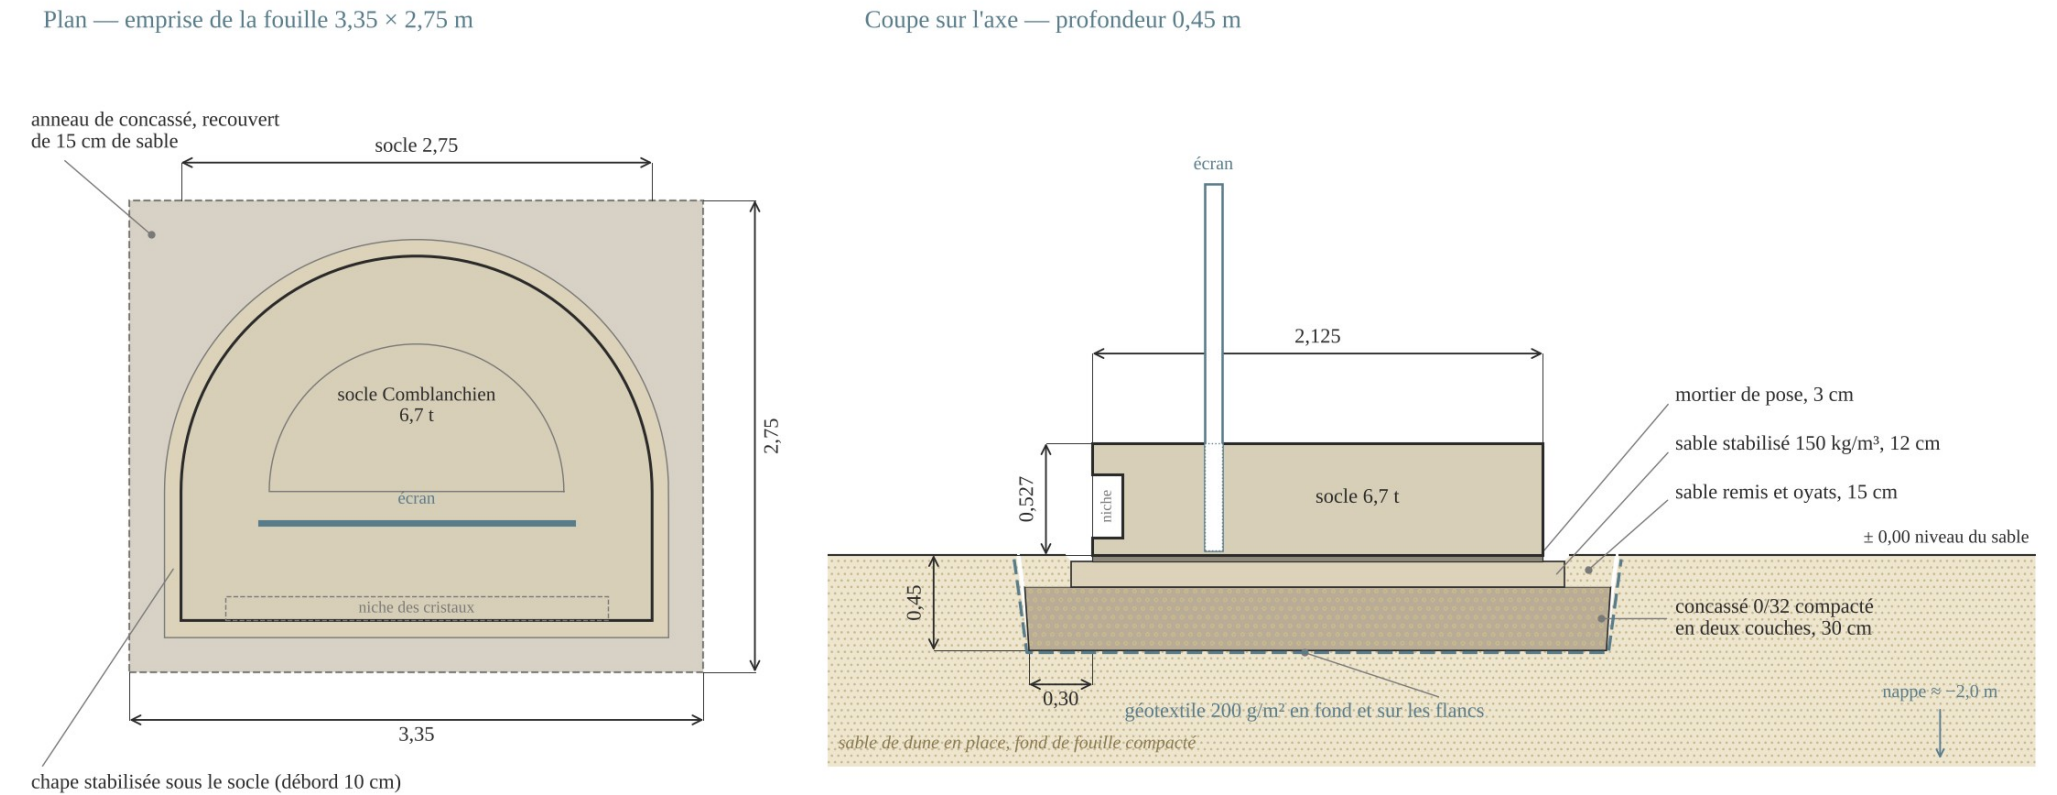

Pression nette au sol 12,2 kPa · tassement à 15 ans 0,6 à 1,7 mm · pente induite ≤ 0,06 % (seuil accepté 1 %) · portance sous vent extrême 1,8 (sable lâche) · coût estimé ≈ 2 600 € HTVA

PROJET LES VEILLEURS — Beaufort 27 ARTISTE · MAÎTRE D'ŒUVRE Eva L'Hoest · +32 495 57 92 12 · eva.lhoest@gmail.com ASSISTANT ÉLECTROMÉCANIQUE Gioacchino Miceli · +32 497 84 45 10 · gioacchino.miceli@thefactory.com	DOCUMENT Fondation — variante A OBJET Lit de concassé et chape stabilisée : plan et coupe N° DOCUMENT · RÉVISION · DATE · HEURE LV-FO-SCH-02 · rév. A · 09-10-2026 15:54 EN LIGNE base-les-veilleurs.vercel.app/les-veilleurs-fondation/	STATUT ESQUISSE © Eva L'Hoest 2026 — Confidentiel. Reproduction, diffusion ou usage hors de cette consultation interdits sans accord écrit de l'artiste. Cotes non contractuelles.
--	--	---